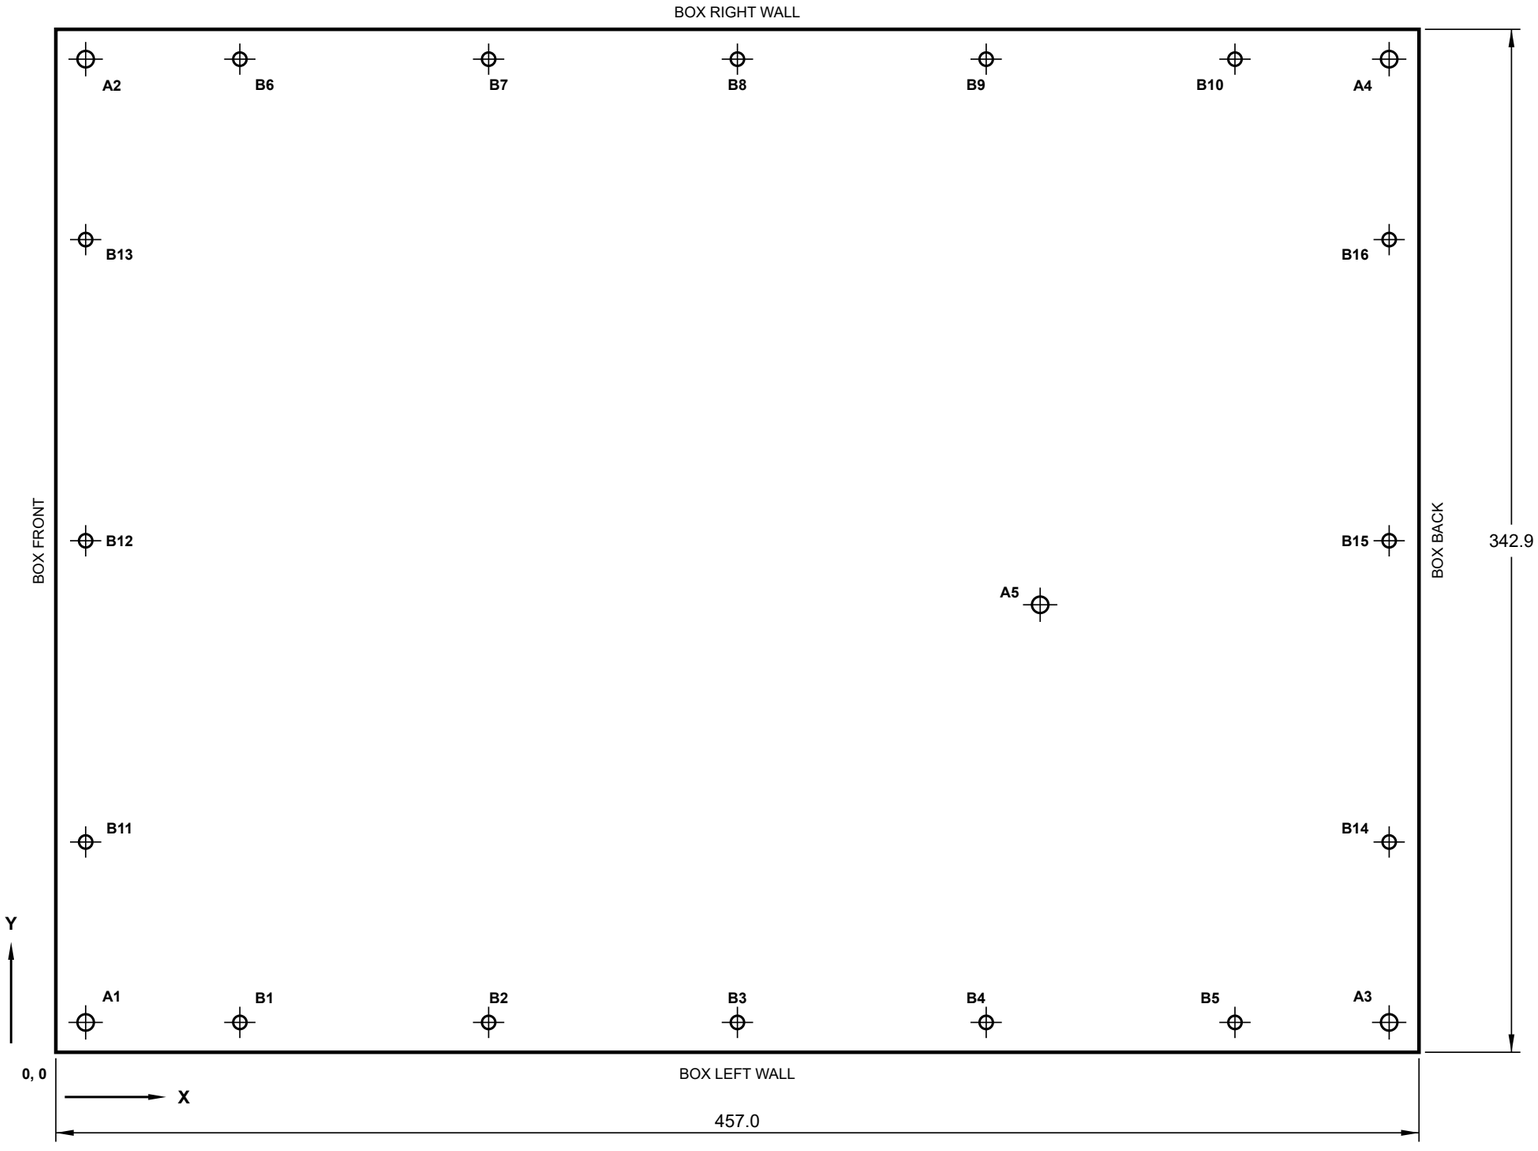


VIEW AS IN THE DXF, SCALE 1:2

REV	DESCRIPTION	DATE	BY
A	FIRST RELEASE, ISSUE #213	2026-10-27	AG

HOLE AND SLOT CHART

TAG	X	Y	SIZE
A1	10.00	10.00	Ø5.5 THRU
A2	10.00	332.90	Ø5.5 THRU
A3	447.00	10.00	Ø5.5 THRU
A4	447.00	332.90	Ø5.5 THRU
A5	330.00	150.00	Ø5.5 THRU
B1	61.70	10.00	Ø4.5 THRU
B2	145.10	10.00	Ø4.5 THRU
B3	228.50	10.00	Ø4.5 THRU
B4	311.90	10.00	Ø4.5 THRU
B5	395.30	10.00	Ø4.5 THRU
B6	61.70	332.90	Ø4.5 THRU
B7	145.10	332.90	Ø4.5 THRU
B8	228.50	332.90	Ø4.5 THRU
B9	311.90	332.90	Ø4.5 THRU
B10	395.30	332.90	Ø4.5 THRU
B11	10.00	70.48	Ø4.5 THRU
B12	10.00	171.45	Ø4.5 THRU
B13	10.00	272.42	Ø4.5 THRU
B14	447.00	70.48	Ø4.5 THRU
B15	447.00	171.45	Ø4.5 THRU
B16	447.00	272.42	Ø4.5 THRU

X, Y: CENTER FROM THE ORIGIN 0, 0, THE NOMINAL LOWER LEFT CORNER.
DATUMS: NOTE 3.
21 HOLES, ALL THRU.

NOTES

1. DIMENSIONS IN MILLIMETERS. THE PLATE IS 457.0 X 342.9 (17.99 X 13.50 IN). DO NOT SCALE THIS DRAWING.
2. MAKE FROM deck_base_plate.dxf (MILLIMETERS, LAYER CUT, IN THE FRAME OF THIS VIEW) BY ANY PROCESS THAT HOLDS THE TOLERANCES: CNC PUNCH, LASER, WATERJET OR MILL. REPORT ANY DIFFERENCE BETWEEN THE FILE AND THIS DRAWING BEFORE CUTTING.
3. DATUMS: THE CENTERS OF HOLES A1 (X 10.00, Y 10.00) AND A3 (Y 10.00). MEASURE EVERY CENTER AND EDGE FROM THEM, NOT FROM THE CUT EDGES. EACH EDGE LIES ON ITS NOMINAL LINE OR UP TO 0.5 INSIDE IT, NEVER OUTSIDE.
4. ALL HOLES AND SLOTS THRU. DEBURR EVERY EDGE, HOLE AND SLOT ON BOTH FACES.
5. NO ANODIZE, PAINT OR COATING: THE PLATE IS BONDED TO PROTECTIVE EARTH THROUGH ITS BARE METAL.
6. MARK "RMR-CB-DECK-BASE REV A" IN PERMANENT INK ON THE FACE SHOWN, NEAR THE ORIGIN.
7. THE CUSTOMER MAY SUPPLY THE MATERIAL AS ONE 18 X 24 IN SHEET OF 5052: USE IT AS SUPPLIED, NO CERTIFICATE NEEDED. CUT THE PLATE FROM ONE CORNER AND RETURN THE REST IN ONE PIECE: THE LOWER BACK PANEL, 342.9 X 87.6, IS CUT FROM IT LATER.
8. FOR ASSEMBLY: THE VIEW SHOWS THE UNDERSIDE AS INSTALLED (X FROM THE BOX'S FRONT TO ITS BACK, Y FROM ITS LEFT WALL TO ITS RIGHT). THE HOLES FOR THE DIN RAILS, DUCTS AND GROUND BARS ARE DRILLED AT ASSEMBLY (SHEET 4); A5, THE PE STUD, IS THE FIRST SCREW OF A GROUND BAR.

UNLESS OTHERWISE SPECIFIED:

DIMENSIONS IN MILLIMETERS
CENTERS ±0.15 FROM A1, A3
HOLE, SLOT SIZES +0.2 / -0
EDGES +0 / -0.5 (NOTE 3)
DEBURR ALL EDGES

DO NOT SCALE DRAWING

TITLE: **DECK PLATE, BASE** — RMR CONTROL BOX

MATERIAL: AL 5052-H32 SHEET, 0.063 IN (1.59 MM), ASTM B209

FINISH: NONE, MILL FINISH: NO ANODIZE, PAINT OR COATING

DWG NO: **RMR-CB-DECK-BASE** — REV: **A**

SIZE	SCALE	QTY	SHEET
B	1:2	1	1 OF 1

DRAWN	DATE	CHECKED
A. GOGOJ	2026-10-27	