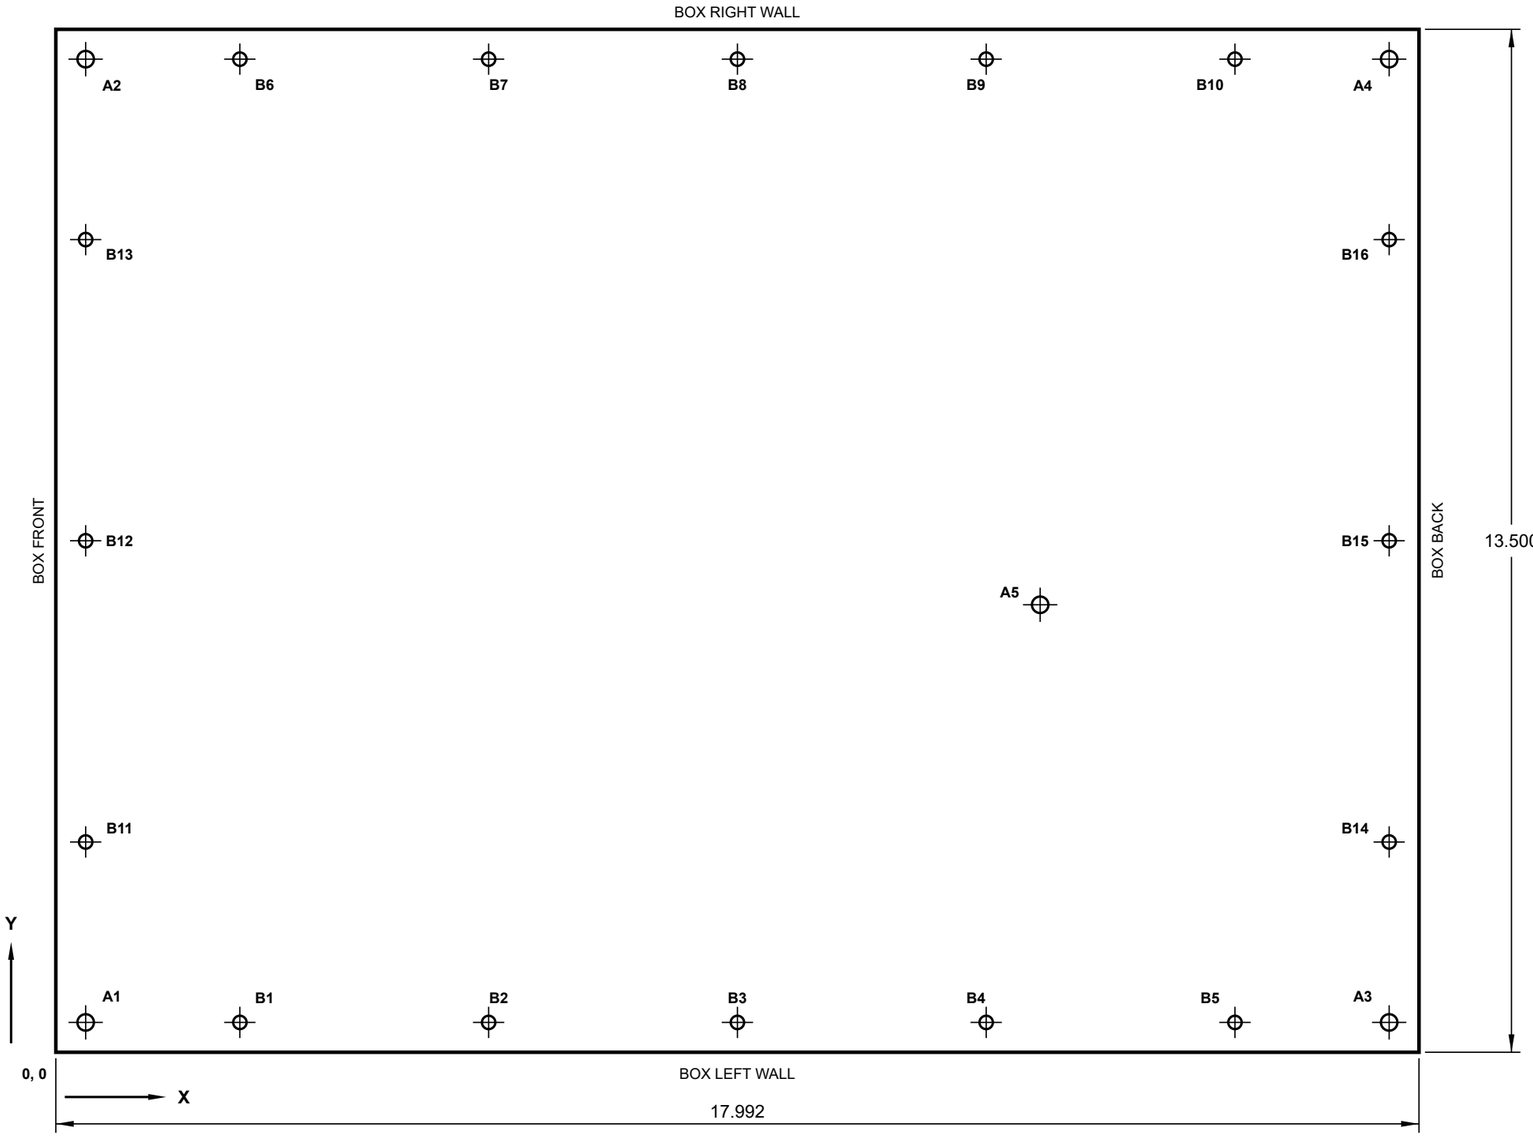


VIEW AS IN THE DXF, SCALE 1:2

REV	DESCRIPTION	DATE	BY
A	FIRST RELEASE, ISSUE #213	2026-10-27	AG

HOLE AND SLOT CHART

TAG	X	Y	SIZE
A1	.394	.394	Ø.217 THRU
A2	.394	13.106	Ø.217 THRU
A3	17.598	.394	Ø.217 THRU
A4	17.598	13.106	Ø.217 THRU
A5	12.992	5.906	Ø.217 THRU
B1	2.429	.394	Ø.178 THRU
B2	5.713	.394	Ø.178 THRU
B3	8.996	.394	Ø.178 THRU
B4	12.280	.394	Ø.178 THRU
B5	15.563	.394	Ø.178 THRU
B6	2.429	13.106	Ø.178 THRU
B7	5.713	13.106	Ø.178 THRU
B8	8.996	13.106	Ø.178 THRU
B9	12.280	13.106	Ø.178 THRU
B10	15.563	13.106	Ø.178 THRU
B11	.394	2.775	Ø.178 THRU
B12	.394	6.750	Ø.178 THRU
B13	.394	10.725	Ø.178 THRU
B14	17.598	2.775	Ø.178 THRU
B15	17.598	6.750	Ø.178 THRU
B16	17.598	10.725	Ø.178 THRU

X, Y: CENTER FROM THE ORIGIN 0, 0, THE NOMINAL LOWER LEFT CORNER.
DATUMS: NOTE 3.
21 HOLES, ALL THRU.

NOTES

1. DIMENSIONS IN INCHES. THE PLATE IS NOMINALLY 17.992 X 13.500 (EDGES: NOTE 3). CONVERTED FROM DRAWING RMR-CB-DECK-BASE (MILLIMETERS), WHICH GOVERNS: EVERY TOLERANCE ZONE HERE LIES INSIDE ITS ZONE THERE.
2. MAKE FROM deck_base_plate.dxf (MILLIMETERS, LAYER CUT, IN THE FRAME OF THIS VIEW) BY ANY PROCESS THAT HOLDS THE TOLERANCES: CNC PUNCH, LASER, WATERJET OR MILL. THE FILE IS ON THE MILLIMETER LIMITS (HOLES AND SLOTS AT THEIR LEAST, THE OUTLINE AT ITS LARGEST), JUST OUTSIDE THESE: OFFSET THE CUT INTO THEM. REPORT ANY OTHER DIFFERENCE OVER .001 BEFORE CUTTING.
3. DATUMS: THE CENTERS OF HOLES A1 (X .394, Y .394) AND A3 (Y .394). MEASURE EVERY CENTER AND EDGE FROM THEM, NOT FROM THE CUT EDGES. EACH EDGE LIES .001 TO .019 INSIDE ITS NOMINAL LINE.
4. ALL HOLES AND SLOTS THRU. DEBURR EVERY EDGE, HOLE AND SLOT ON BOTH FACES.
5. NO ANODIZE, PAINT OR COATING: THE PLATE IS BONDED TO PROTECTIVE EARTH THROUGH ITS BARE METAL.
6. MARK THE PART NUMBER "RMR-CB-DECK-BASE REV A" IN PERMANENT INK ON THE FACE SHOWN, NEAR THE ORIGIN.
7. THE CUSTOMER MAY SUPPLY THE MATERIAL AS ONE 18 X 24 IN SHEET OF 5052: USE IT AS SUPPLIED, NO CERTIFICATE NEEDED. CUT THE PLATE FROM ONE CORNER AND RETURN THE REST IN ONE PIECE: THE LOWER BACK PANEL, 13.500 X 3.448, IS CUT FROM IT LATER.
8. FOR ASSEMBLY: THE VIEW SHOWS THE UNDERSIDE AS INSTALLED (SEE THE EDGE LABELS). THE HOLES FOR THE DIN RAILS, DUCTS AND GROUND BARS ARE DRILLED AT ASSEMBLY (SHEET 4); A5, THE PE STUD, IS THE FIRST SCREW OF A GROUND BAR.

UNLESS OTHERWISE SPECIFIED:

DIMENSIONS IN INCHES
CENTERS ±.005 FROM A1, A3
HOLE, SLOT SIZES +.006 / -.000
EDGES -.001 / -.019 (NOTE 3)
DEBURR ALL EDGES

DO NOT SCALE DRAWING

TITLE: RMR CONTROL BOX

DECK PLATE, BASE

MATERIAL: AL 5052-H32 SHEET, .063 THICK, ASTM B209

FINISH: NONE, MILL FINISH: NO ANODIZE, PAINT OR COATING

DWG NO	REV
RMR-CB-DECK-BASE-IN	A

SIZE	SCALE	QTY	SHEET
B	1:2	1	1 OF 1

DRAWN	DATE	CHECKED
A. GOGOJ	2026-10-27	